GU ららぽーと富士見店（2413区画）積算根拠図

元図：施工図一式（A03 平面図・A04 床伏図・A05 天井伏図・照明器具表・A16〜A21 展開図）／縮尺 1/200 を通り芯基準で 1m グリッド読み取り

■ 図面拾い 数量集計

LGS ST100（㎡）	332.1
LGS ST65 両面間仕切（㎡）	344.2
柱 LGS＋PB（㎡）	105.0
PB12.5（壁・柱・下がり壁, ㎡）	1157.9
A工事壁 直接仕上げ（㎡）	67.1
床 ES3001（売場＋レジ＋FRブース外, ㎡）	854.8
床 P-41（BOH＋SW, ㎡）	194.7
天井 AEP（全室, ㎡）	1063.9
柱巻きミラー（本 / 面）	7 本 / 14 枚

■ 壁仕上げ（面積・展開図による面別）

AEP N-87	555.1 ㎡
黒クロス LW-4207	79.5 ㎡
素地	265.6 ㎡
白クロス LW-4630/4635	152.7 ㎡
化粧PB（木目・桐）	109.1 ㎡

■ 収録ページ


1. 床仕上げ範囲（A04 床伏図）
2. 壁 下地・仕上げ範囲（A03 平面図）
3. 天井仕上げ範囲（A05 天井伏図）
4. 照明器具 台数（照明配置図）
5. コンセント・弱電 台数（コンセント配置図）

6〜9. 展開図 ↔ 壁ID 対応（A16〜A19）

・室面積は平面図の面積表（正式値）で計上。図上概算は確認用（差 ±10% 程度）。
・壁長さは通り芯からの図上読み取り。高さは CH3,750（SW は 3,155、下がり壁 650）。
・器具・コンセントは照明器具表の総数量で計上（配置図と目視照合）。
・GU 支給品（照明器具・床材・什器・サイン）は施工費のみ。
・見積 v2（2021実績数量ベース）との差は 確認用HTML の比較表を参照。

積算根拠図 ｜ 1. 床仕上げ範囲

A04 床伏図に重ね描き。売場・レジ・FRブース外＝ES3001-45（材料GU支給）、BOH・SW＝P-41、FRブース内＝WBH-603。灰色＝階段室（A工事・対象外）

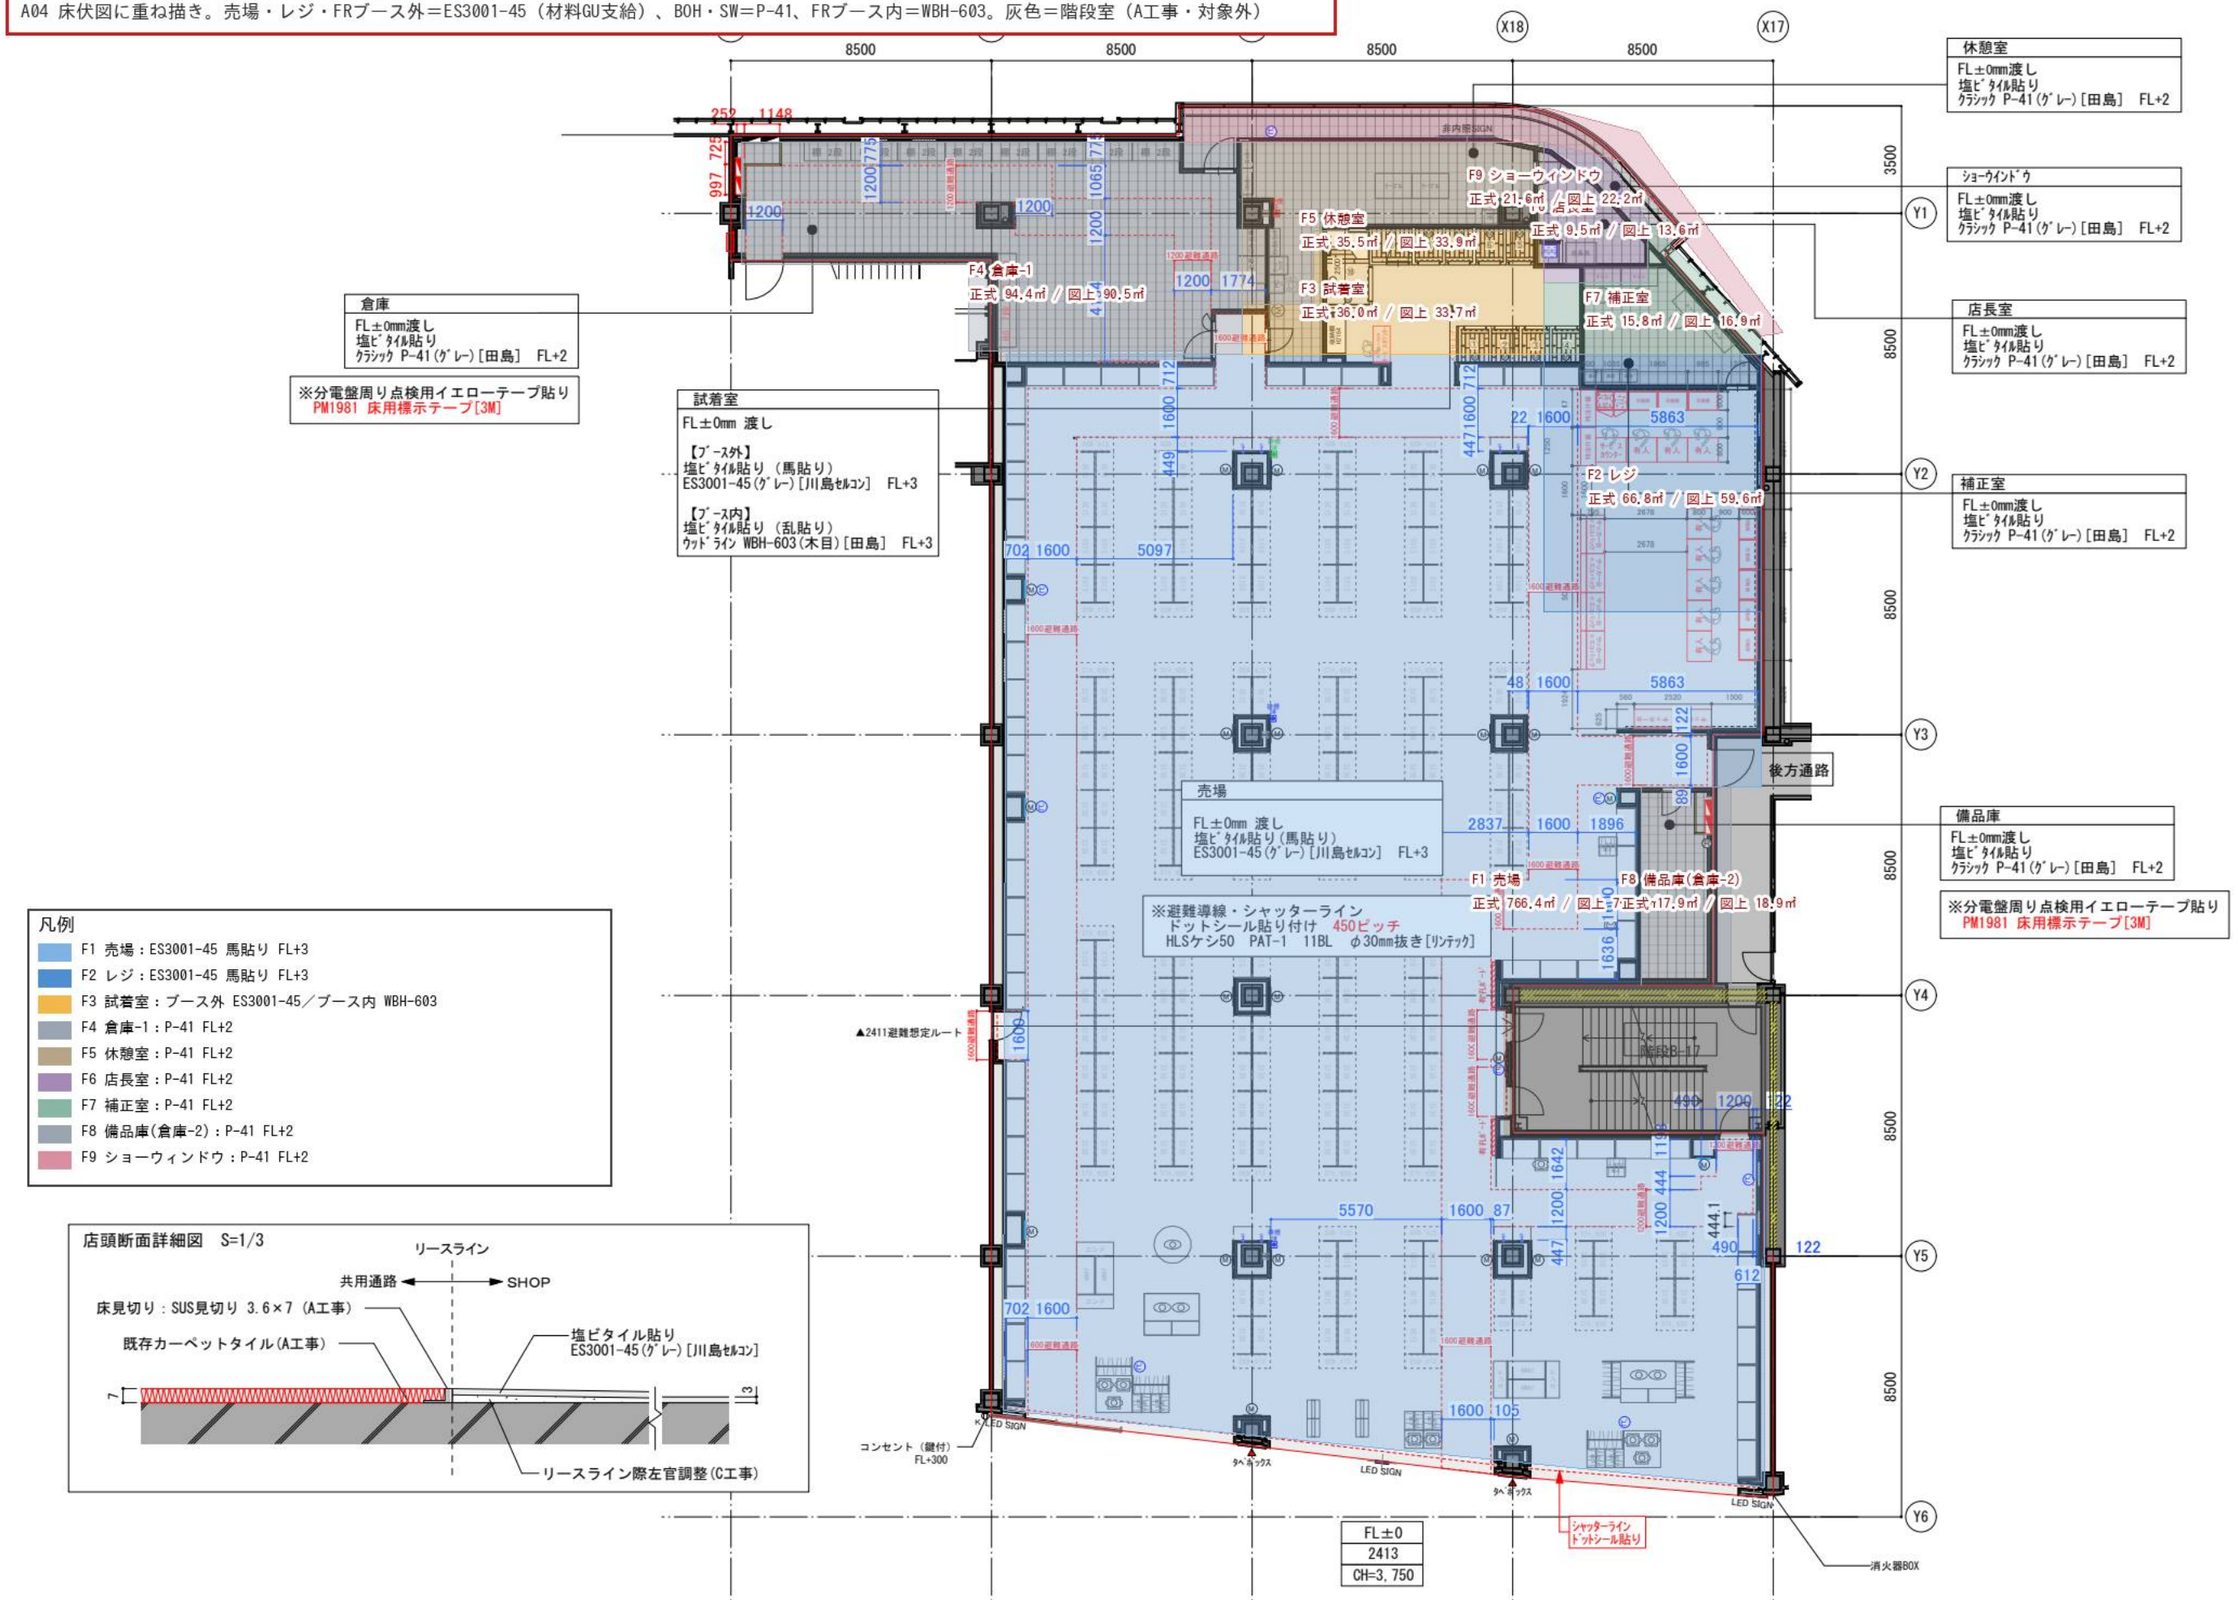

凡例

- F1 売場：ES3001-45 馬貼り FL+3
- F2 レジ：ES3001-45 馬貼り FL+3
- F3 試着室：ブース外 ES3001-45／ブース内 WBH-603
- F4 倉庫-1：P-41 FL+2
- F5 休憩室：P-41 FL+2
- F6 店長室：P-41 FL+2
- F7 補正室：P-41 FL+2
- F8 備品庫(倉庫-2)：P-41 FL+2
- F9 ショーウィンドウ：P-41 FL+2

店頭断面詳細図 S=1/3


PLAN-A-2-3

space SPACE CO., LTD. www.space-tokyo.co.jp	TITLE 2413区画 / CH=3750 ｼﾞｭｰららぽーと富士見店 新装工事	SUBJECTS 床伏図	SCALE 1/200 (A3)	DRAWER shimane CHECK ishizaka	DATE 20.07.20 / 20.07.27 / 20.07.30 / 20.08.06 / 20.08.21 / 20.08.28 20.09.07 / 20.09.11 / 20.10.02 / 20.10.29 / 20.11.12 /20.11.19 20.11.27 / 20.12.03 / 20.12.10 / 20.12.14 /20.12.22 / 21.01.25 21.03.02 / 21.04.06	DRAWING No. A04

積算根拠図 ｜ 2. 壁 下地・仕上げ範囲

A03 平面図に重ね描き。線色＝仕上げ（青 AEP N-87／黒 黒クロス／橙 白クロス／茶 化粧PB／灰 素地・A工事壁／桃 SW／緑 下がり壁）。緑枠＝柱巻きミラー対象柱 7本


TOTAL AREA			1063.6㎡	322坪	100%
SALES AREA			766.4㎡	232坪	72%
CASH REGISTER AREA(ﾚｼﾞ)			66.8㎡	20坪	6%
SHOW WINDOW(ｼｮｰｳｲﾝﾄﾞｳ)			21.6㎡	7坪	2%
	CASHWRAP	8			
BOH	FITTING ROOM(試着室)		36.0㎡	11坪	3%
	ALTERATION ROOM(補正室)		15.8㎡	5坪	1%
	STOCK ROOM-1(倉庫)		94.4㎡	29坪	9%
	STOCK ROOM-2(備品庫)		17.9㎡	5坪	2%
	STAFF BREAK ROOM(休憩室)		35.5㎡	11坪	3%
	MANAGER'S OFFICE(店長室)		9.5㎡	3坪	1%
BOH/TOTAL AREA			208.9㎡	63坪	20%

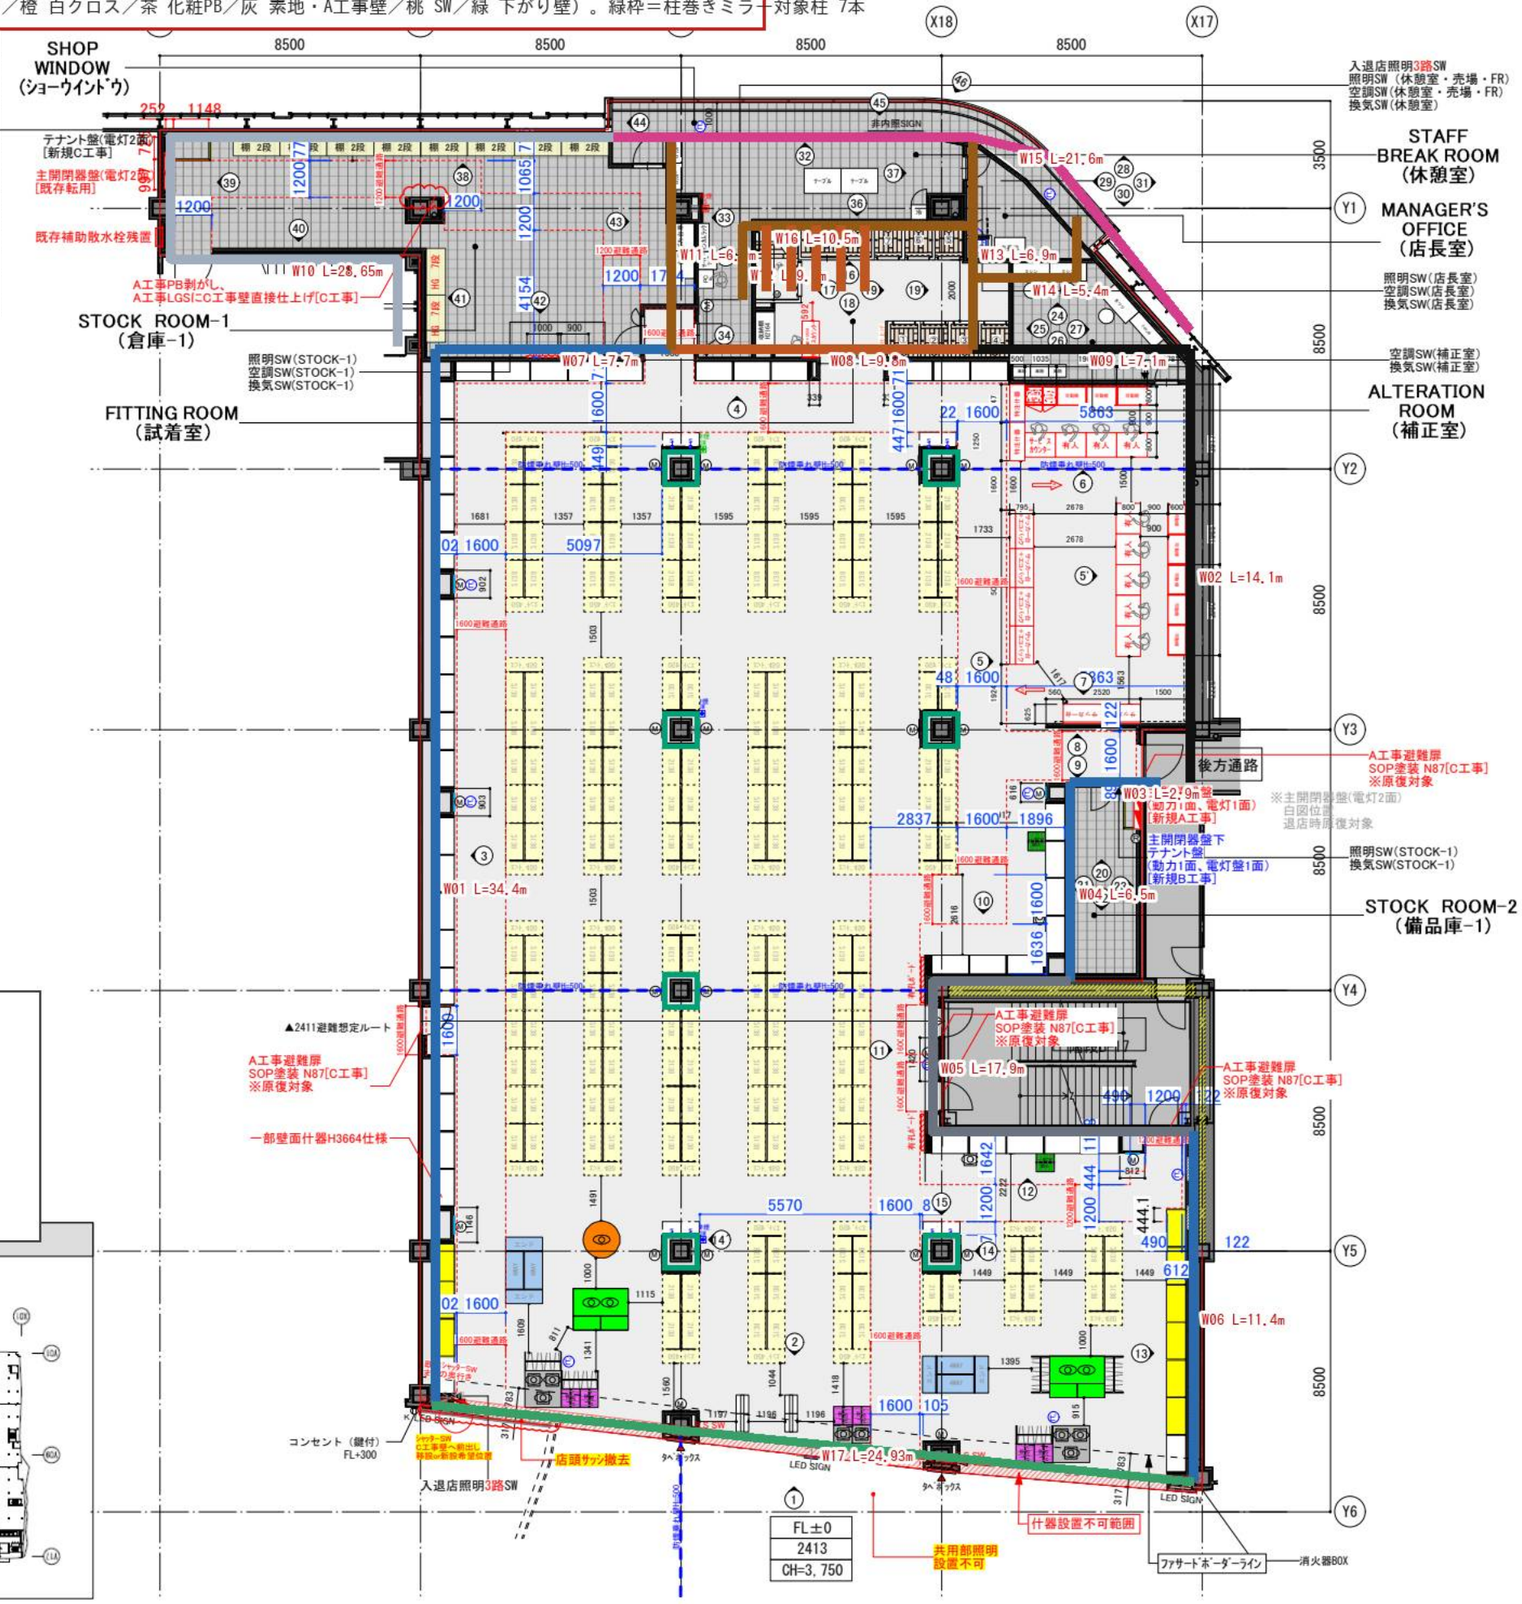

凡例（壁）


- AEP N-87 3分ツヤ（売場・補正室・SW）
- 黒クロス LW-4207（レジ背面・右壁）
- 白クロス LW-4630/4635（試着室）
- 化粧PB 木目・桐（休憩室・店長室）
- 素地＋ワイド巾木H300（倉庫）
- A工事壁 直接仕上げ（階段室）
- ショーウィンドウ背面（CH3,155）
- 店頭 下がり壁 H650

■ショーケース

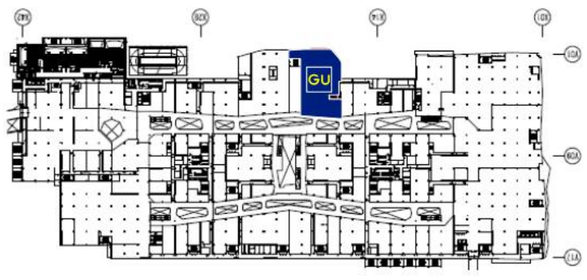


■壁面什器高さ　S＝1/60

■壁面什器断面図

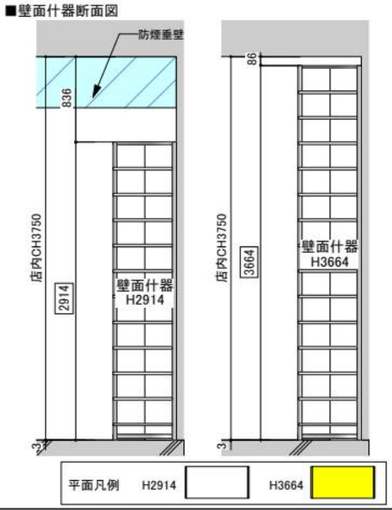


■ファサード展開図　S＝1/60

※レギュレーション参照

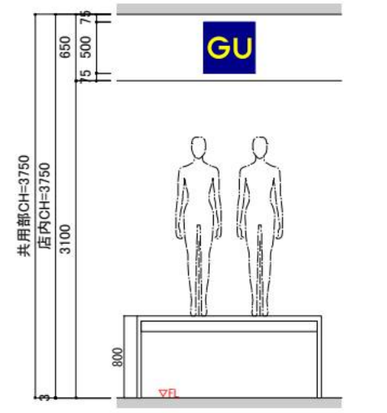

■ファサードボーダー断面図　S＝1/60

※レギュレーション参照

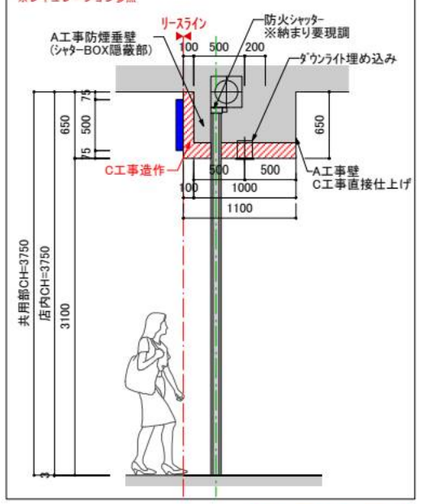


PLAN-A-2-3

space SPACE CO., LTD. www.space-tokyo.co.jp	TITLE 2413区画 / CH=3750 ジーユーららぽーと富士見店 新装工事	SUBJECTS 平面図	SCALE 1/200 (A3)	DRAWER shimane CHECK ishizaka	DATE 20.07.20 / 20.07.27 / 20.07.30 / 20.08.06 / 20.08.21 / 20.08.28 20.09.07 / 20.09.11 / 20.10.02 / 20.10.29 / 20.11.12 /20.11.19 20.11.27 / 20.12.03 / 20.12.10 / 20.12.14 /20.12.22 / 21.01.25 21.03.02 / 21.04.06	DRAWING No. A03

積算根拠図 ｜ 3. 天井仕上げ範囲

A05 天井伏図。全室 既存A工事天井転用＋AEP N-95（1063.9㎡）。店長室のみ 天井PB不燃12.5 貼替＋AEP。SW は CH3,155

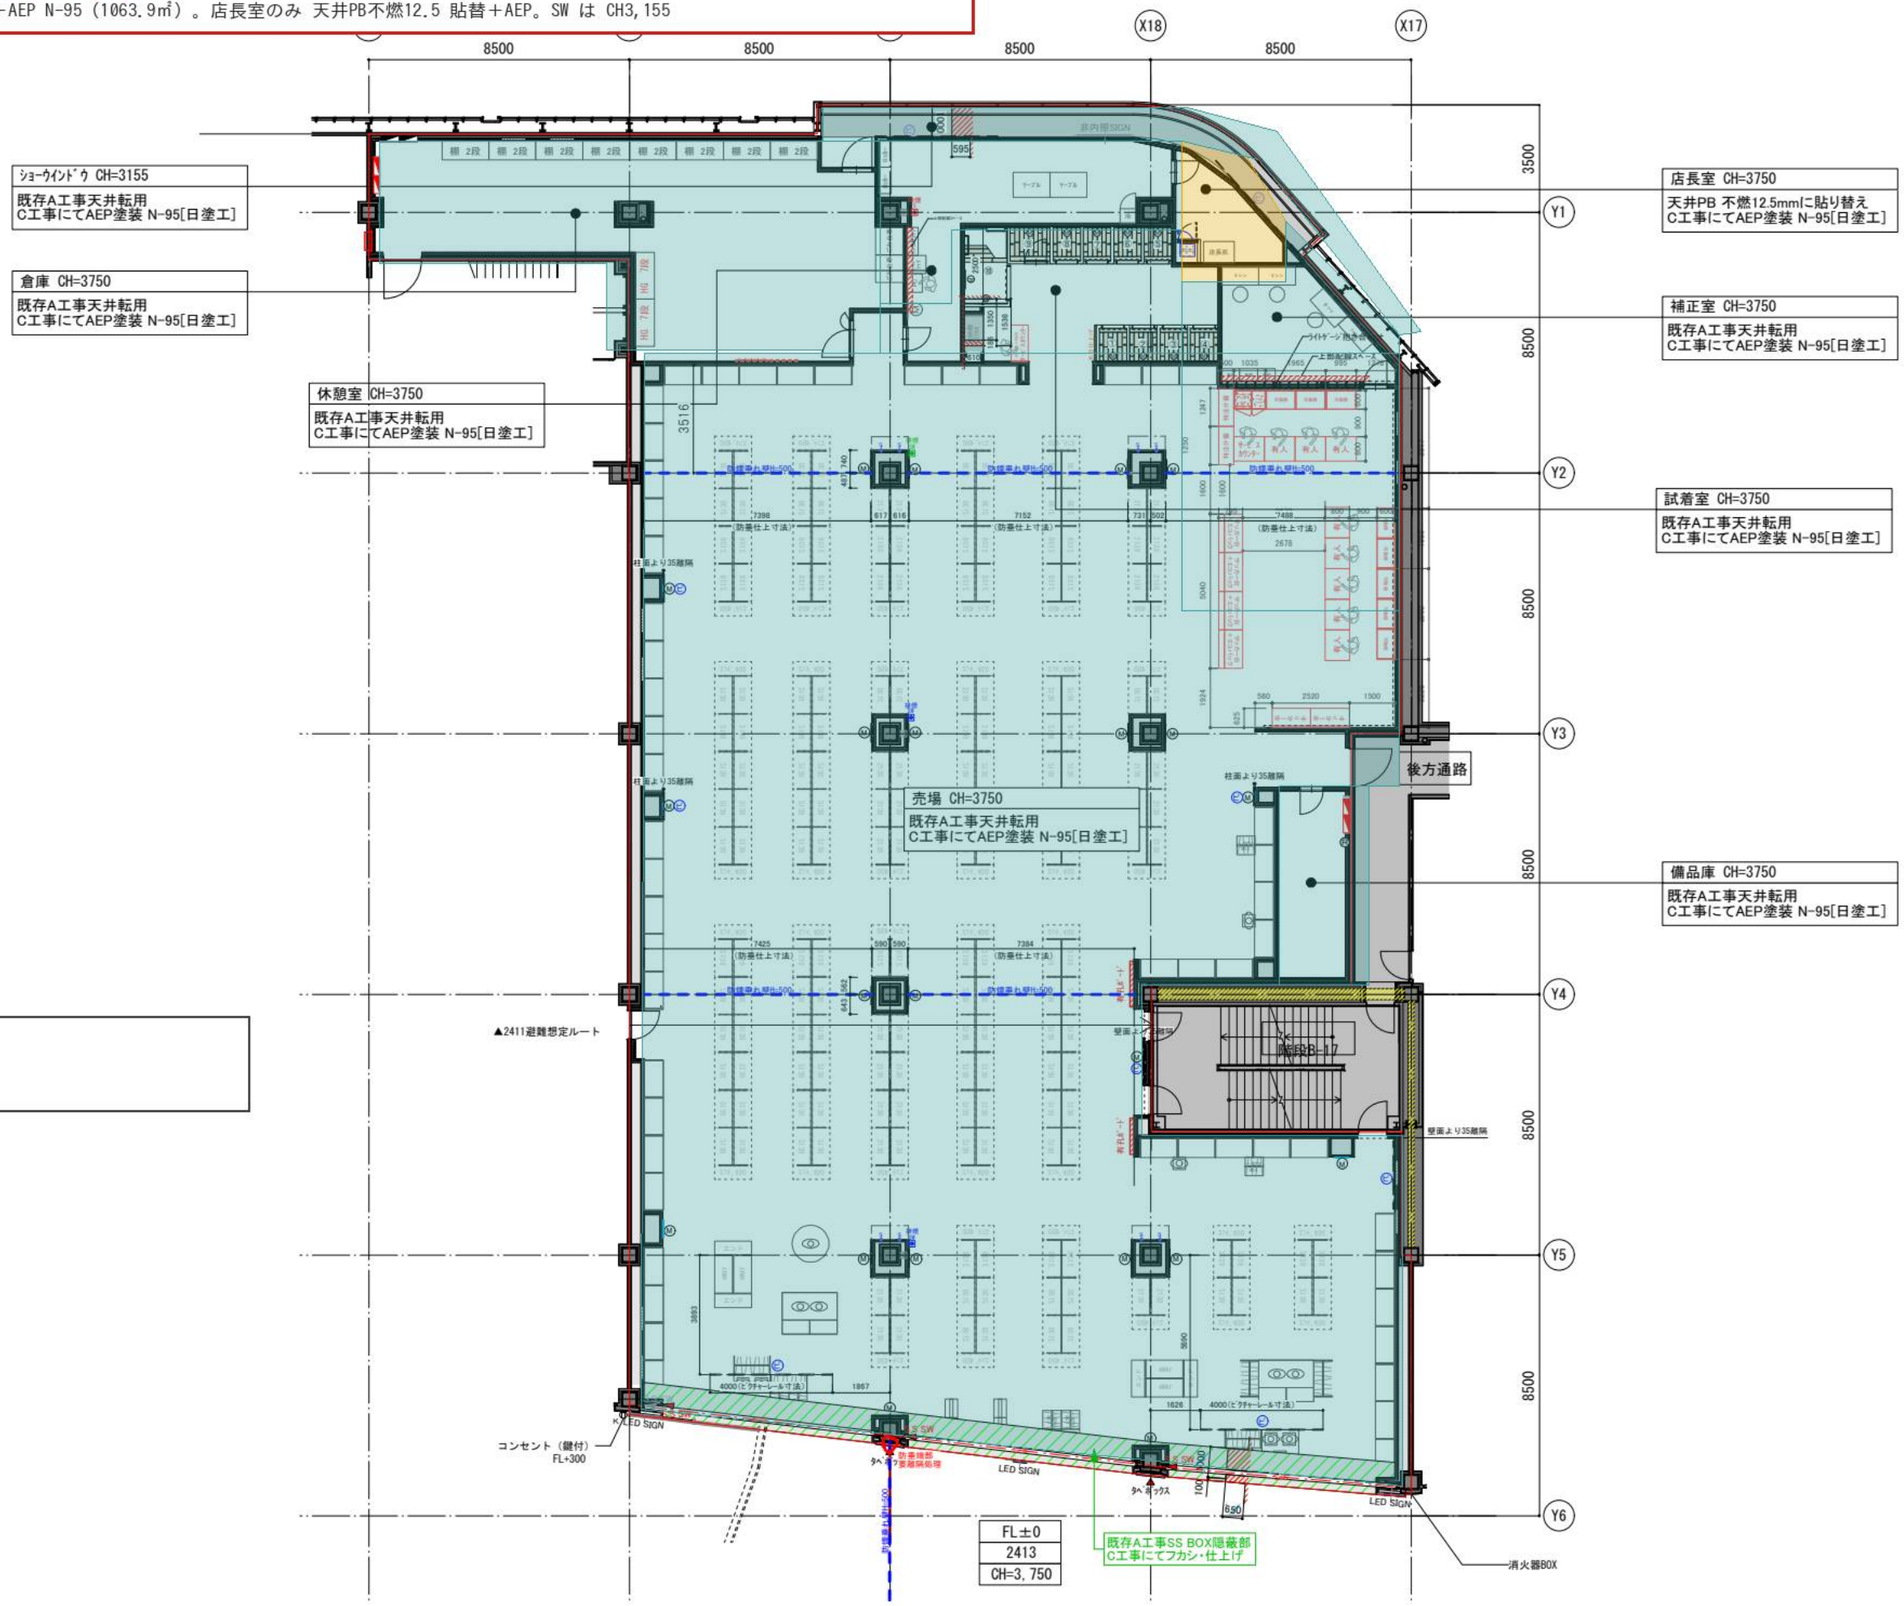

凡例（天井）


- 既存天井転用＋AEP N-95 ツヤ消し
- 店長室：PB12.5 貼替＋AEP

PLAN-A-2-3

space SPACE CO., LTD. www.space-tokyo.co.jp	TITLE 2413区画 / CH=3750 ｼﾞｭｰららぽーと富士見店 新装工事	SUBJECTS 天井伏図	SCALE 1/200 (A3)	DRAWER shimane CHECK ishizaka	DATE 20.07.20 / 20.07.27 / 20.07.30 / 20.08.06 / 20.08.21 / 20.08.28 20.09.07 / 20.09.11 / 20.10.02 / 20.10.29 / 20.11.12 /20.11.19 20.11.27 / 20.12.03 / 20.12.10 / 20.12.14 /20.12.22 / 21.01.25 21.03.02 / 21.04.06	DRAWING No. A05

積算根拠図 ｜ 4. 照明器具 台数

照明配置図。器具は GU 支給（シマダ手配）→ 開口・取付・配線・落下防止ワイヤーのみ計上

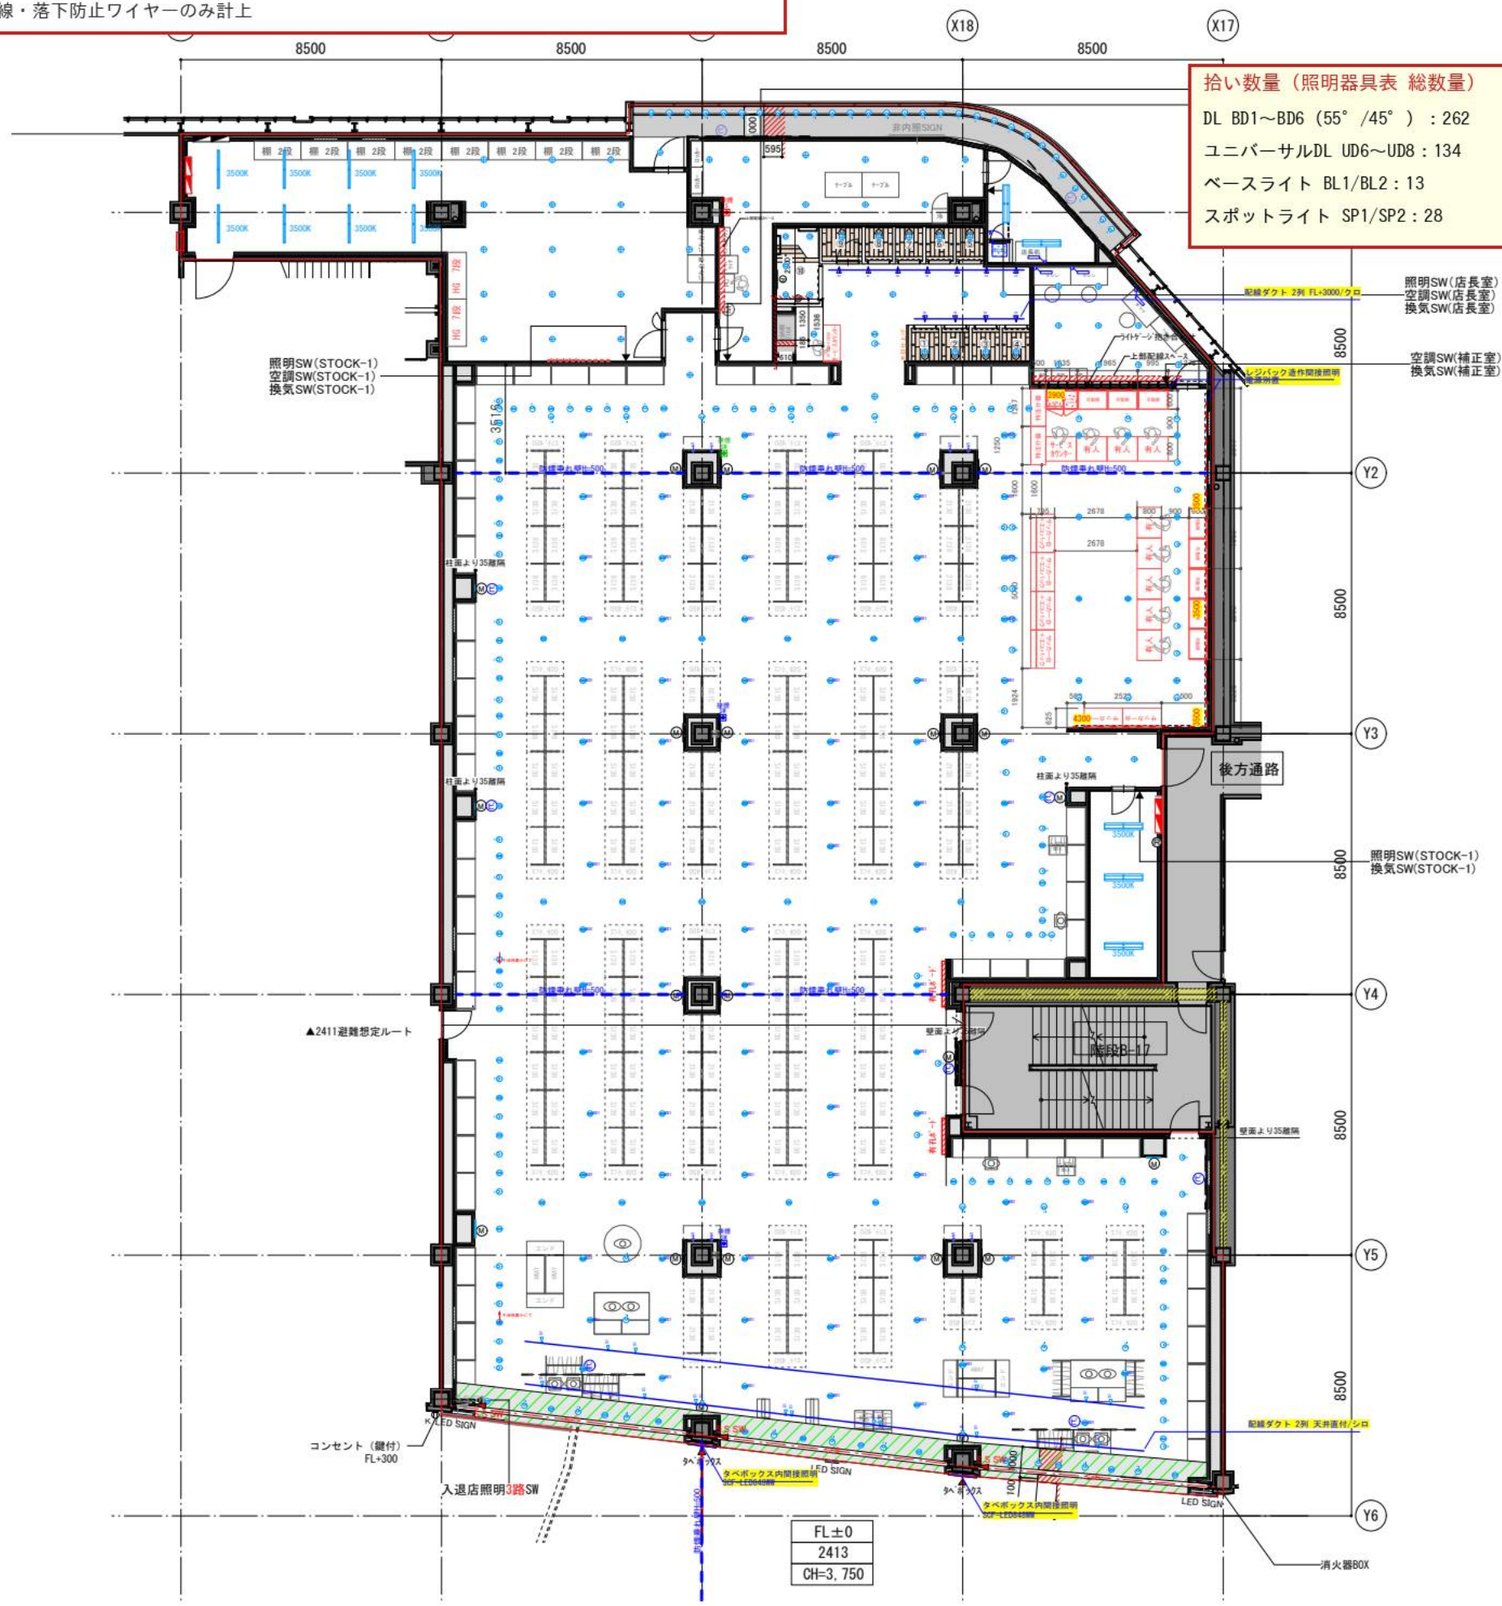

拾い数量（照明器具表 総数量）

DL BD1～BD6（55°/45°）：262

ユニバーサルDL UD6～UD8：134

ベースライト BL1/BL2：13

スポットライト SP1/SP2：28

PLAN-A-2-3

space SPACE CO., LTD. www.space-tokyo.co.jp	TITLE 2413区画 / CH=3750 ジューららぽーと富士見店 新装工事	SUBJECTS 照明配置図	SCALE 1/200 (A3)	DRAWER shimane CHECK ishizaka	DATE 20.07.20 / 20.07.27 / 20.07.30 / 20.08.06 / 20.08.21 / 20.08.28 20.09.07 / 20.09.11 / 20.10.02 / 20.10.29 / 20.11.12 /20.11.19 20.11.27 / 20.12.03 / 20.12.10 / 20.12.14 /20.12.22 / 21.01.25 21.03.02 / 21.04.06	DRAWING No. A06a

積算根拠図 ｜ 5. コンセント・弱電 台数

コンセント配置図。取付・配線（材工）で計上。カットリレーはB工事（空配管・電源のみC工事）

※防火区画ではない為、ﾌｧｲﾔｰﾀﾞﾝﾊﾟｰ不要。
（201223技術内監より回答有り）

換気グリル
Ｐ－１８ＧＬ６　1ケ
Ｐ－２３ＧＬ６　2ケ

（平面指示なきシンボルはＰ－１８ＧＬ６）

空調凡例

- 新規EHP[C工事]
- 既存GHP

（凡例）

	電灯A盤
	電源別置型非常灯
	非常放送スピーカー
	煙感知器
	スプリンクラー
	排煙口
	誘導灯
	吸込み口　吹き出し口

音響機器

記号	品番	品名	数量	備考
	WA-HA121	店内アンプ	1	店長室に設置
	WA-260	バックルーム用アンプ	1	
	WS-A12T(トランス内蔵型)	店内天井埋込スピーカー	10	設定は、1KΩ
	WS-M10T-W(トランス内蔵型)	店内天井吊下げスピーカー	2	設定は、1KΩ
	WS-Q146W	店内スピーカー専用金具	2	
		吊下げｽﾋﾟｰｶｰ用特注ﾌﾟﾚｰﾄ	2	
	WS-TN10	バックルームスピーカー	6	3W(3.3kΩ)に切換
	WS-6530	スピーカーパネル	6	
	WZ-VC106	SPコントローラー	7	入口SPにも設置
	WM-530	レジカウンターマイク	1	レジバックカウンター内に設置
	JPP-101A	レジマイク用プレート	1	
	RJ-RU	ICレコーダー用プレート	1	FRに設置

監視カメラ

記号	品番	品名	数量	備考
	SCB-4100D	吊下げ型ダミーカメラ	8	矢印がカメラ方向
	VA-WH-11	カメラ取付台	8	


設備プロット位置：
200710受領白図プロット位置
210212最終設備プロット受領（施工済み）

※ 印の干渉箇所については、設備機器にて配置調整をお願い致します。

※ 印の干渉箇所については、照明機器/AV機器にて配置調整致します。

拾い数量（照明器具表 総数量）

- ダブルコンセント：41
- 抜け止め接地付ダブルコンセント：42
- 天井裏ダブルコンセント：4
- POS/TEL/FAX アウトレット：20

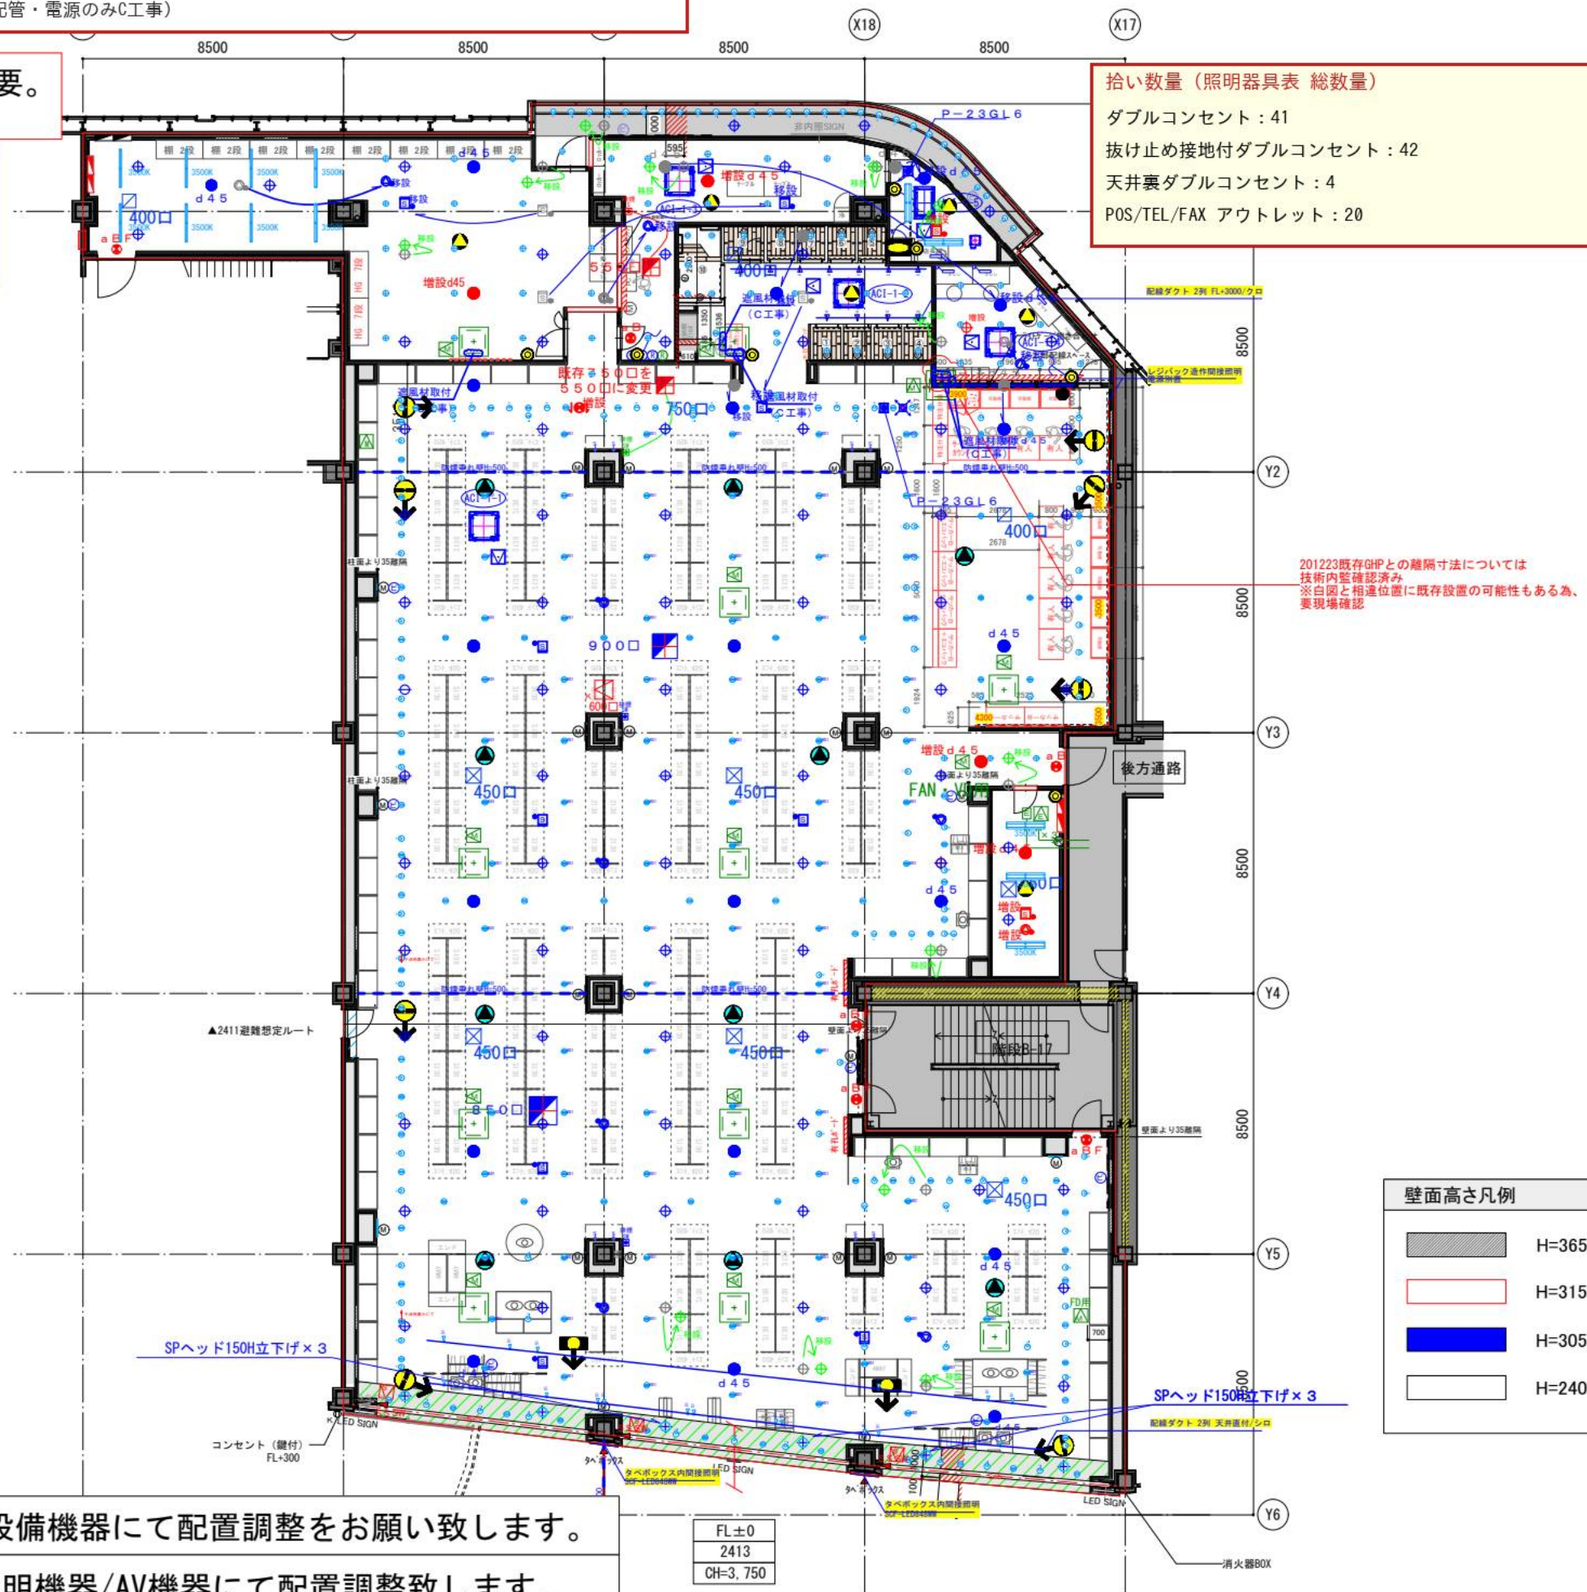

壁面高さ凡例　（FL±0mmより）

- H=3650（天井まで）
- H=3150（上部開口 H=500）
- H=3050（上部開口 H=600）
- H=2400（FR/上部開口 H=1350）

PLAN-A-2-3


space SPACE CO., LTD. www.space-tokyo.co.jp	TITLE 2413区画 / CH=3750 ｼﾞｭｰららぽーと富士見店 新装工事	SUBJECTS 総合天井伏（設備プロット）図	SCALE 1/200 (A3)	DRAWER shimane / CHECK ishizaka	DATE 20.07.20 / 20.07.27 / 20.07.30 / 20.08.06 / 20.08.21 / 20.08.28 / 20.09.07 / 20.09.11 / 20.10.02 / 20.10.29 / 20.11.12 /20.11.19 / 20.11.27 / 20.12.03 / 20.12.10 / 20.12.14 /20.12.22 / 21.01.25 / 21.03.02 / 21.04.06	DRAWING No. A07a


積算根拠図 ｜ 6. 展開図 ⇔ 壁ID 対応


壁の仕上げ種別・高さはこの展開図で確認（面数は確認用HTMLの壁一覧に記載）

W17 店頭下がり壁（展開1・2）

W01 売場左壁（展開3）

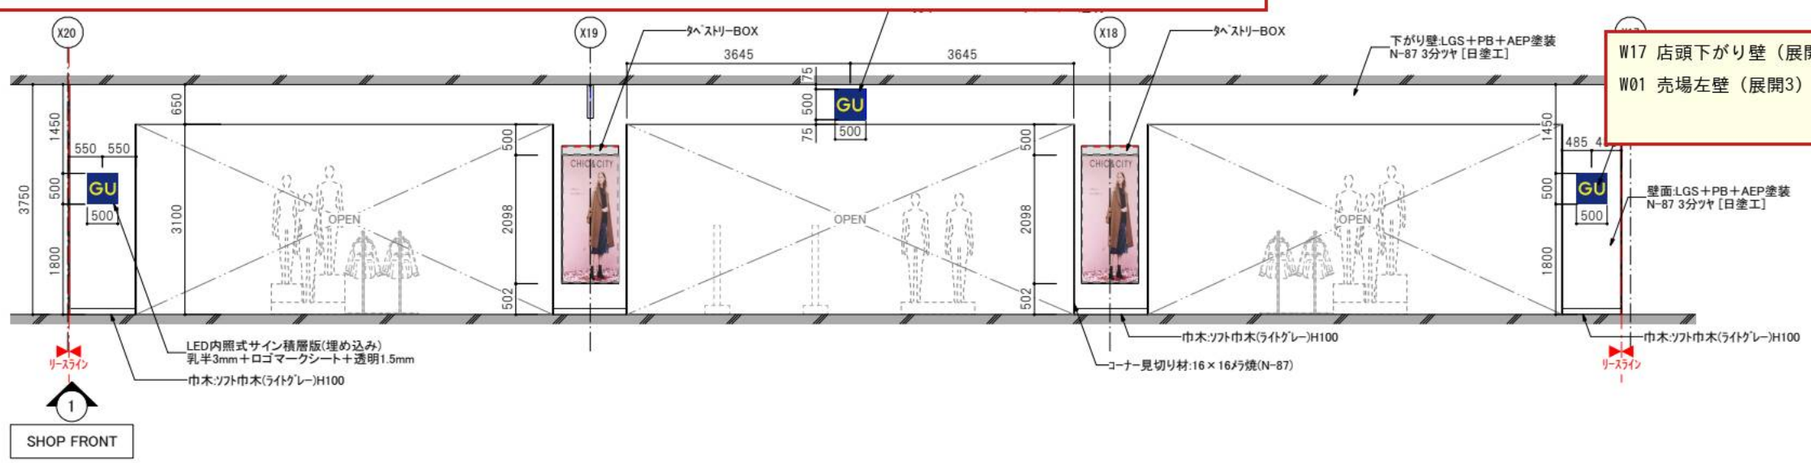

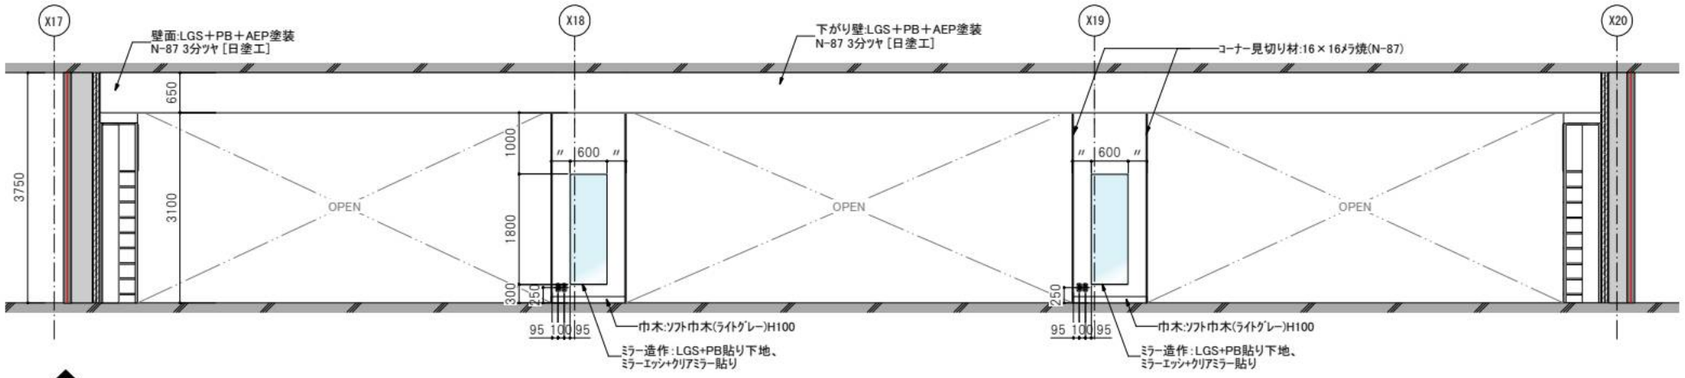

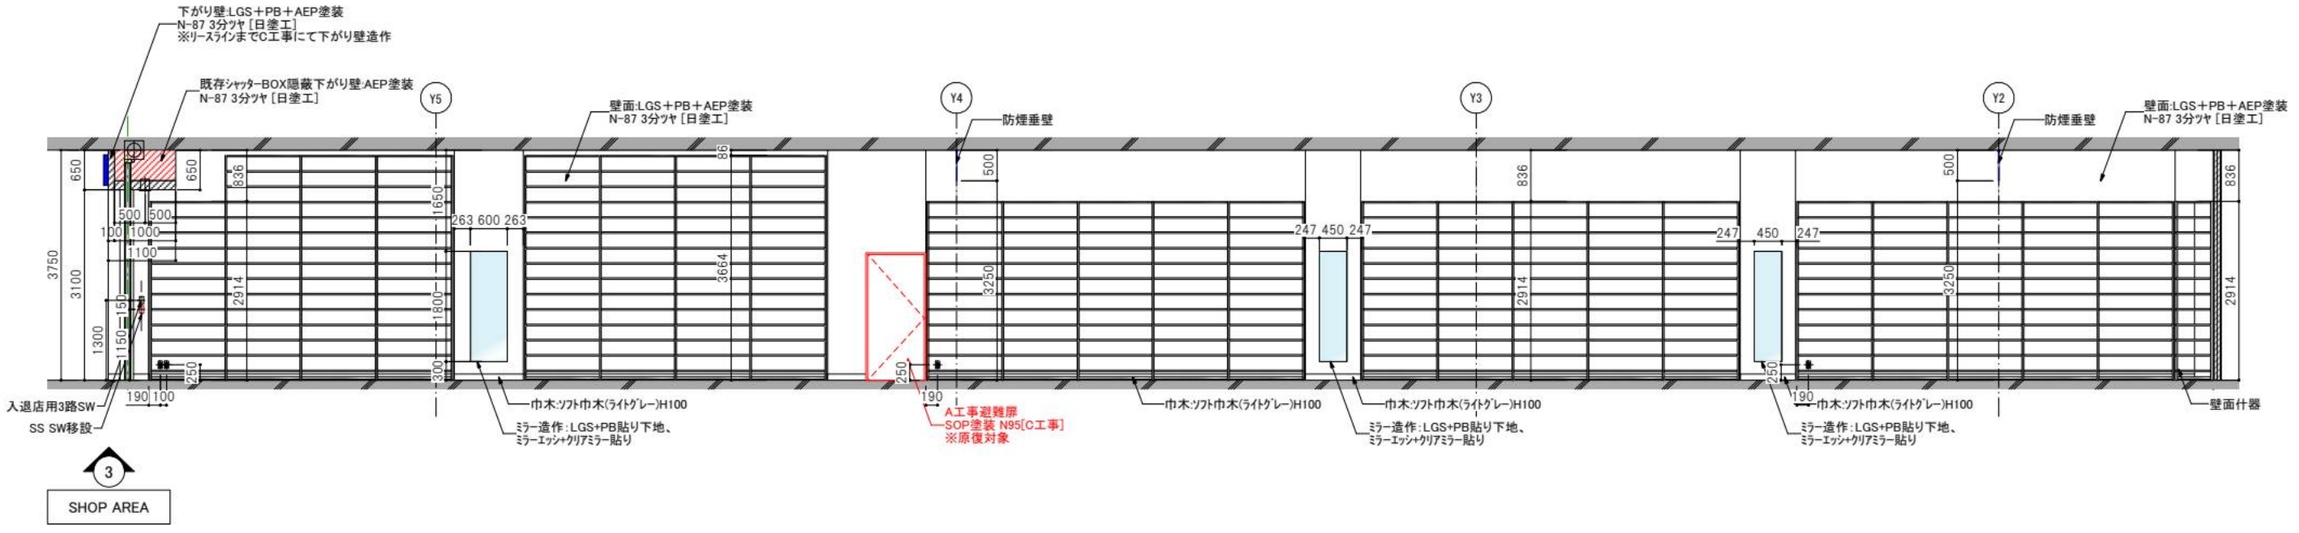


space SPACE CO., LTD. www.space-tokyo.co.jp	TITLE 2413区画 / CH=3750 ジーユーららぽーと富士見店 新装工事	SUBJECTS 展開図-1	SCALE 1/100 (A3)	DRAWER shimane CHECK ishizaka	DATE 2020.10.02 / 2020.11.27 / 2020.12.10 / 2021.01.18 /2021.01.22	DRAWING No. A16

積算根拠図 ｜ 7. 展開図 ⇔ 壁ID 対応


壁の仕上げ種別・高さはこの展開図で確認（面数は確認用HTMLの壁一覧に記載）

W07/W08 奥壁・FR前面（展開4）


W02/W09 レジ 黒クロス（展開5・5'・6・7）

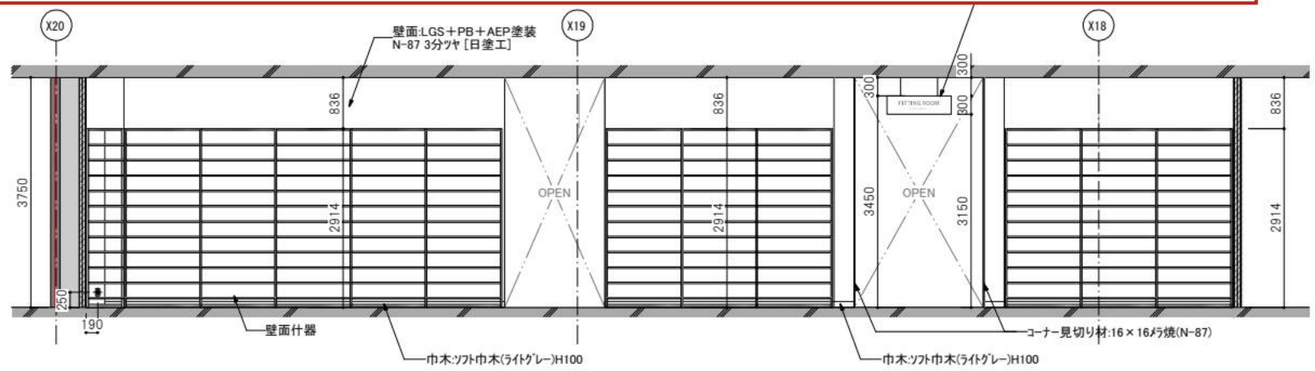


4 SHOP AREA

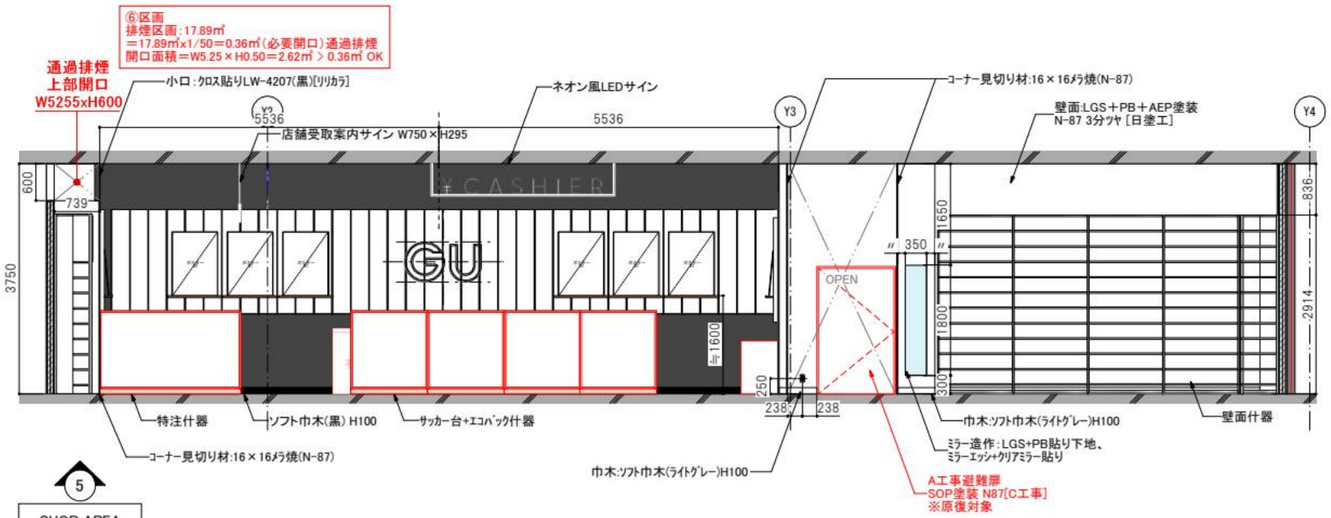

5 SHOP AREA

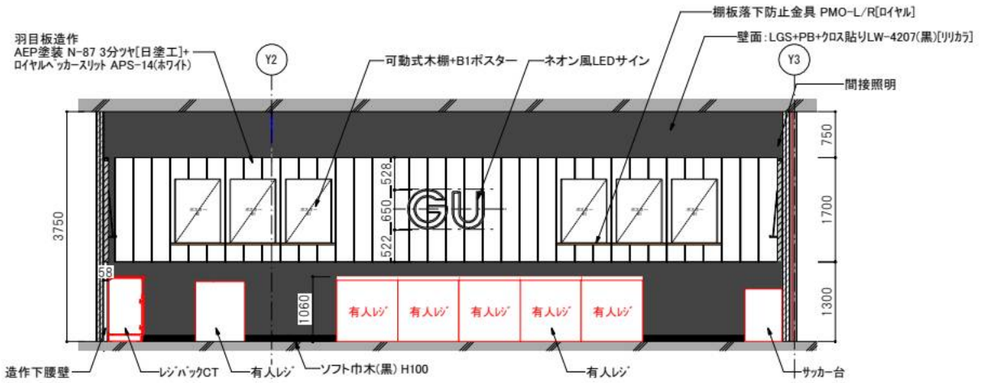


5' SHOP AREA

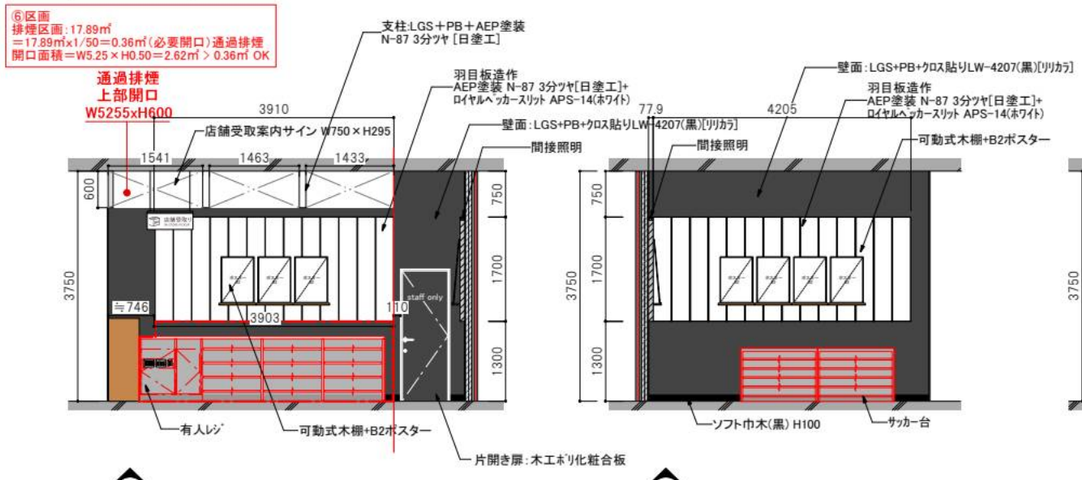


6 SHOP AREA


7 SHOP AREA

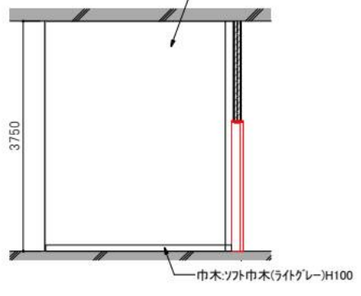

8 SHOP AREA

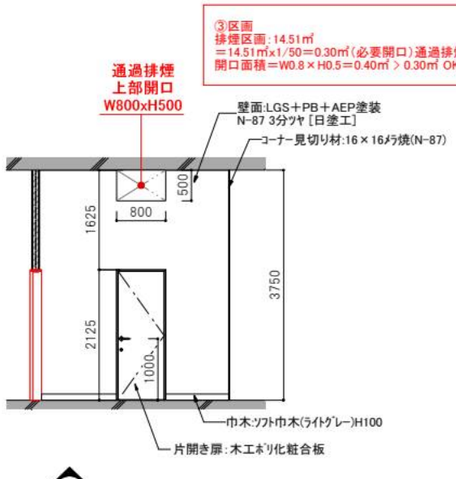

9 SHOP AREA

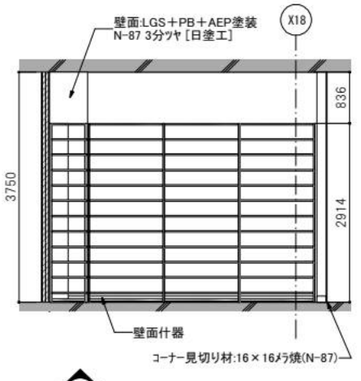


10 SHOP AREA


space SPACE CO., LTD. www.space-tokyo.co.jp	TITLE 2413区画 / CH=3750 ｼﾞｰﾕｰららぽーと富士見店 新装工事	SUBJECTS 展開図-2	SCALE 1/100 (A3)	DRAWER shimane CHECK ishizaka	DATE 2020.10.02 / 2020.11.27 / 2020.12.10 / 2021.01.18 /2021.01.22	DRAWING No. A17


積算根拠図 ｜ 8. 展開図 ⇔ 壁ID 対応


壁の仕上げ種別・高さはこの展開図で確認（面数は確認用HTMLの壁一覧に記載）


W05 階段室 A工事壁（展開11）
W06 右壁 H3664什器（展開13）
W08/W12/W16 試着室 クロス（展開16～19）
W03/W04 備品庫 素地（展開20～22）

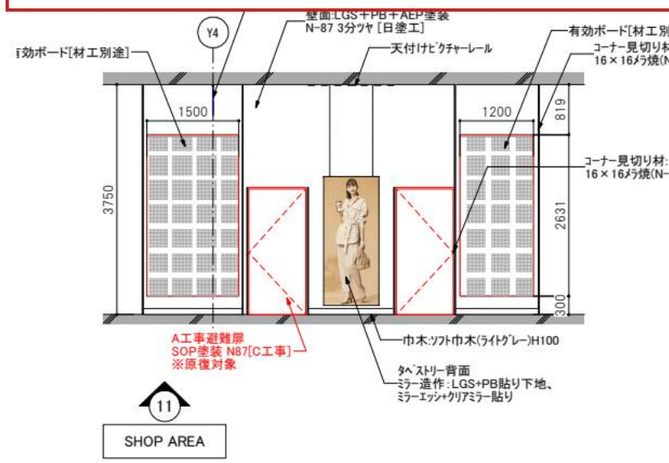


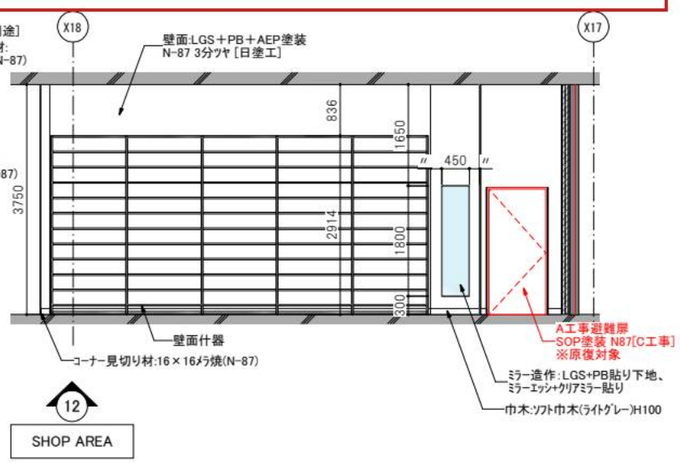


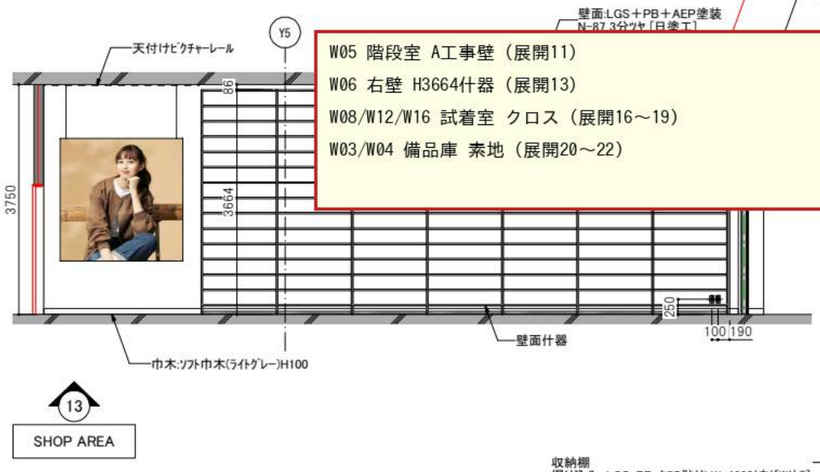


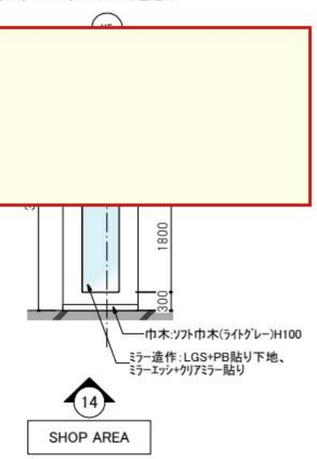


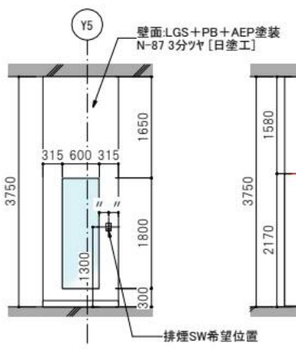

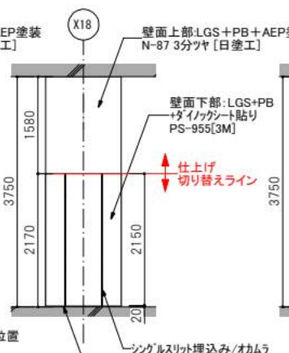


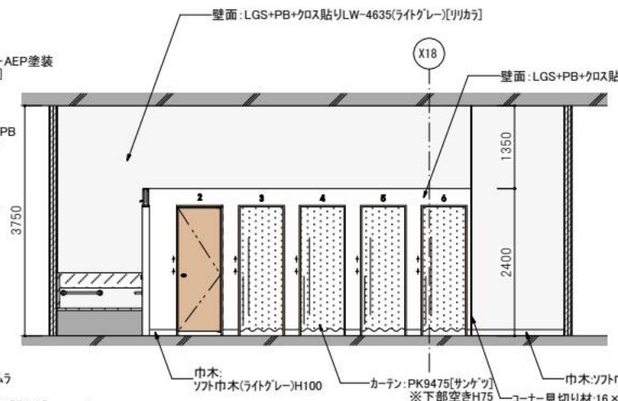


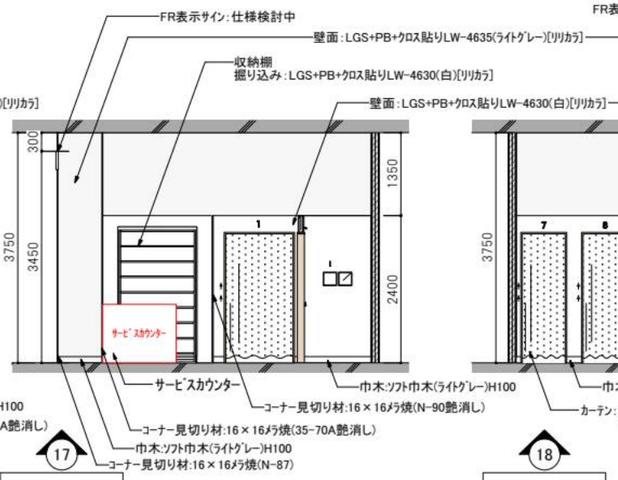


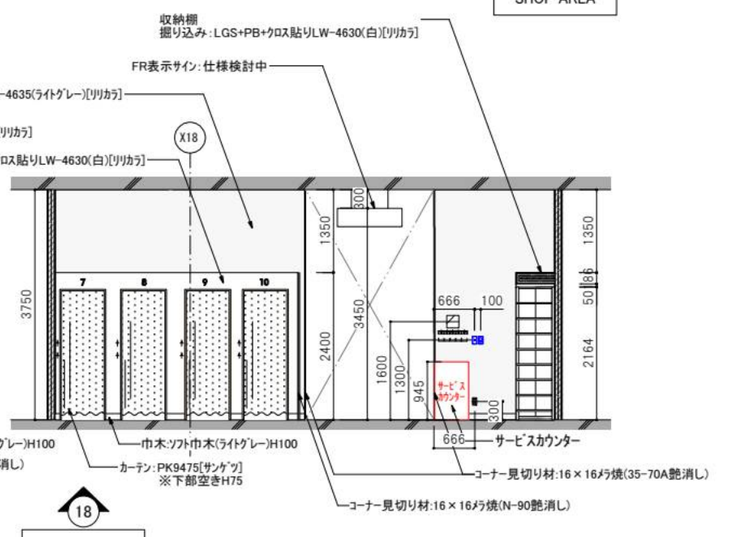



③区画
排煙区画：14.51㎡
＝14.51㎡×1/50＝0.30㎡（必要開口）通過排煙
開口面積＝W0.8×H0.5＝0.40㎡ > 0.30㎡ OK

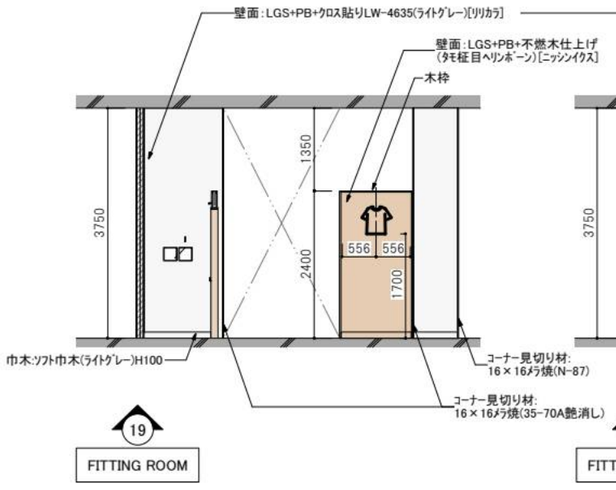

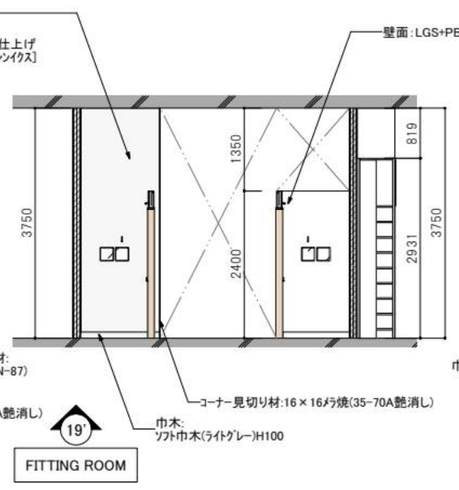

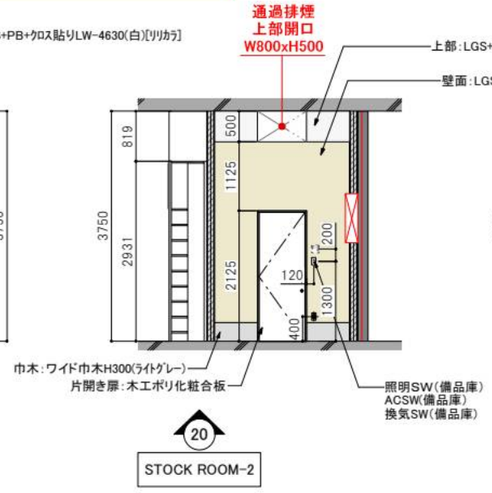

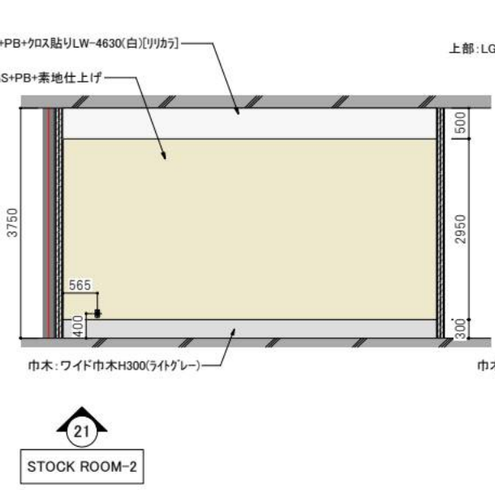

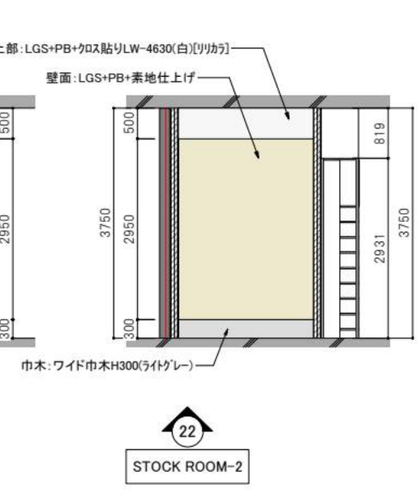


space SPACE CO., LTD. www.space-tokyo.co.jp	TITLE 2413区画 / CH=3750 ｼﾞｰﾕｰららぽーと富士見店 新装工事	SUBJECTS 展開図-3	SCALE 1/100 (A3)	DRAWER shimane CHECK ishizaka	DATE 2020.10.02 / 2020.11.27 / 2020.12.10 / 2021.01.18 /2021.01.22	DRAWING No. A18

積算根拠図 ｜ 9. 展開図 ⇔ 壁ID 対応


壁の仕上げ種別・高さはこの展開図で確認（面数は確認用HTMLの壁一覧に記載）

W09/W13/W14 補正室 AEP（展開24～27）


W11～W14 店長室・休憩室 化粧PB（展開28～36）

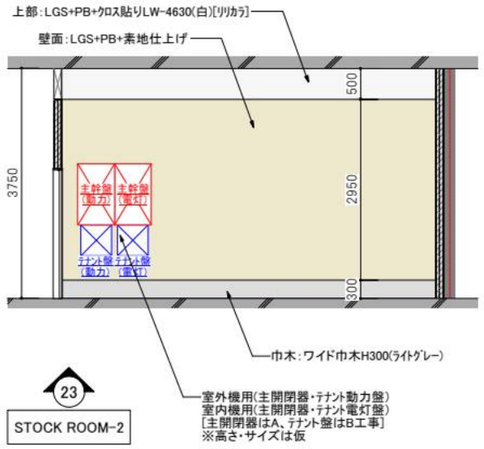


23 STOCK ROOM-2

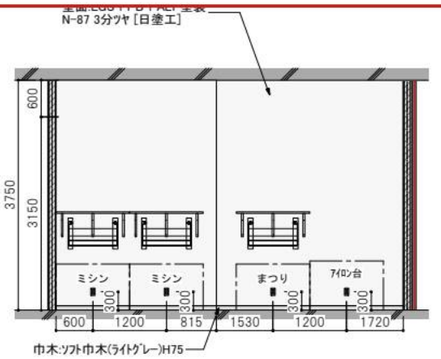


24 ALTERATION ROOM

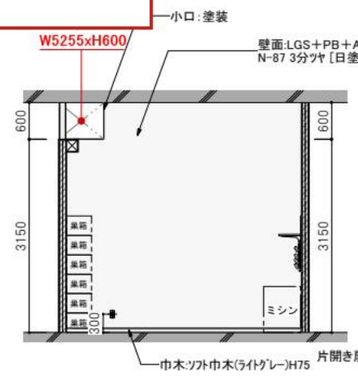


25 ALTERATION ROOM

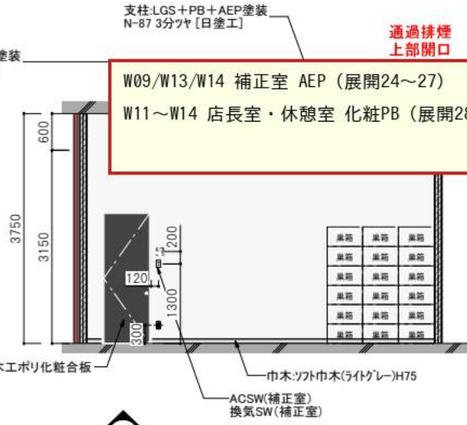

26 ALTERATION ROOM

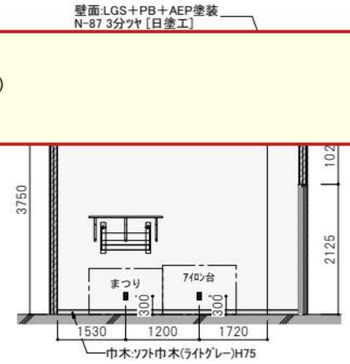


27 ALTERATION ROOM

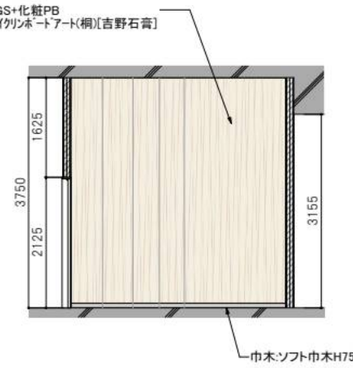


28 MANAGER'S OFFICE




29 MANAGER'S OFFICE

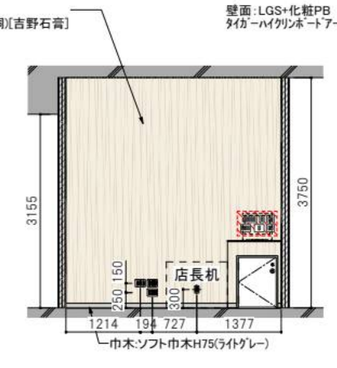

30 MANAGER'S OFFICE

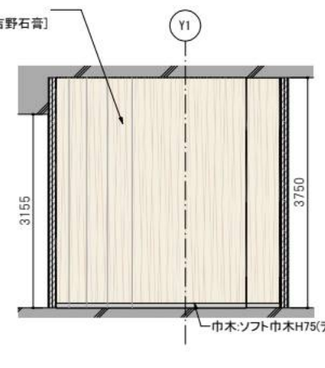


31 MANAGER'S OFFICE

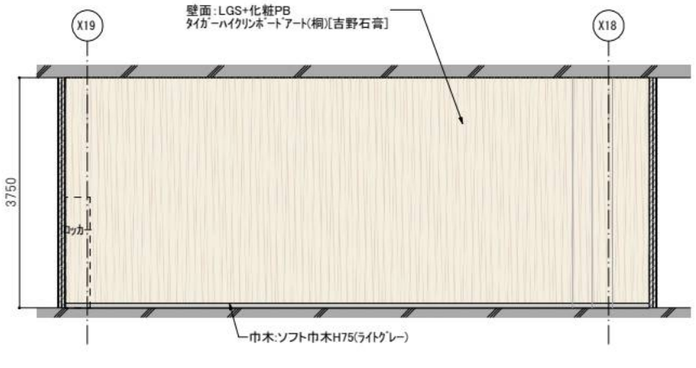


32 STAFF ROOM

⑨区画
排煙区画：89.33㎡
＝89.33㎡×1/50＝1.79㎡（必要開口）通過排煙開口面積＝(W2.58+W1.63)
=W4.21×H0.5=2.10㎡ > 1.79㎡ OK


⑩区画
排煙区画：21.56㎡
＝20.67㎡×1/50＝0.43㎡（必要開口）通過排煙開口面積＝W0.87×H0.5＝0.44㎡ > 0.43㎡ OK

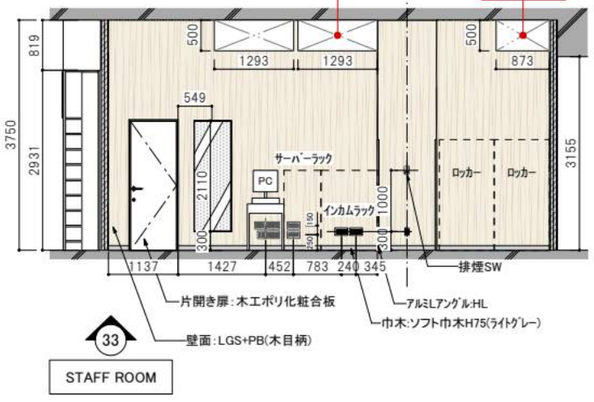


33 STAFF ROOM

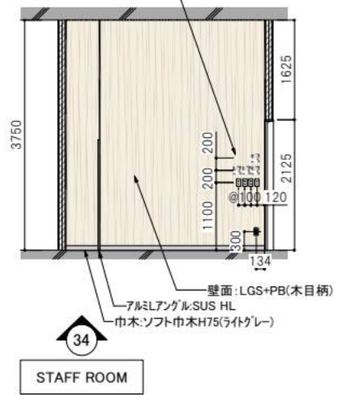

34 STAFF ROOM

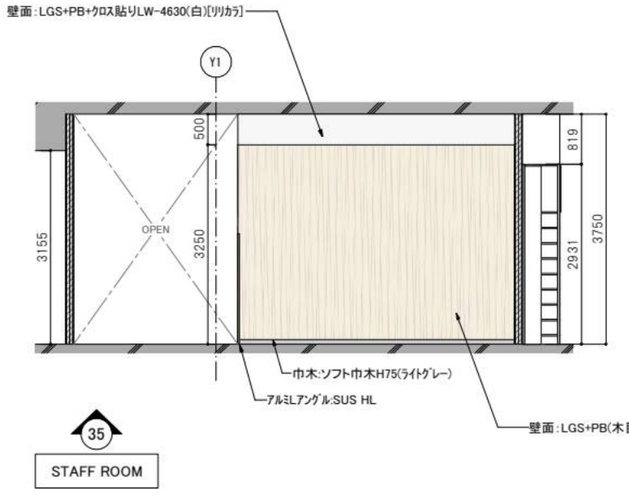

35 STAFF ROOM

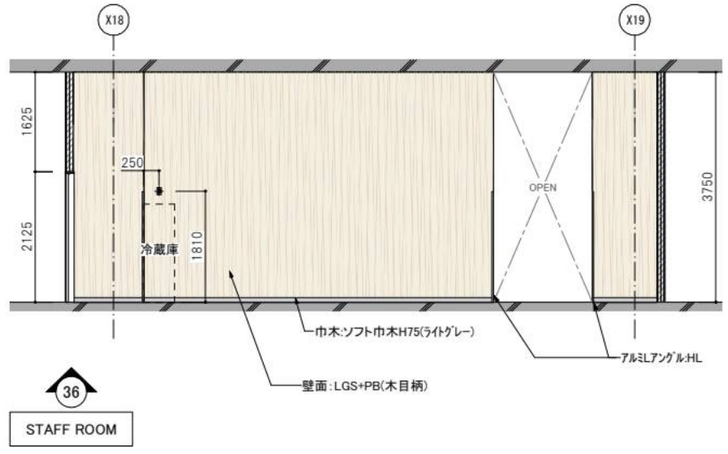

36 STAFF ROOM

SPACE CO., LTD. www.space-tokyo.co.jp	TITLE 2413区画 / CH=3750 ジーユーららぽーと富士見店 新装工事	SUBJECTS 展開図-4	SCALE 1/100 (A3)	DRAWER shimane CHECK ishizaka	DATE 2020.10.02 / 2020.11.27 / 2020.12.10 / 2021.01.18 /2021.01.22	DRAWING No. A19